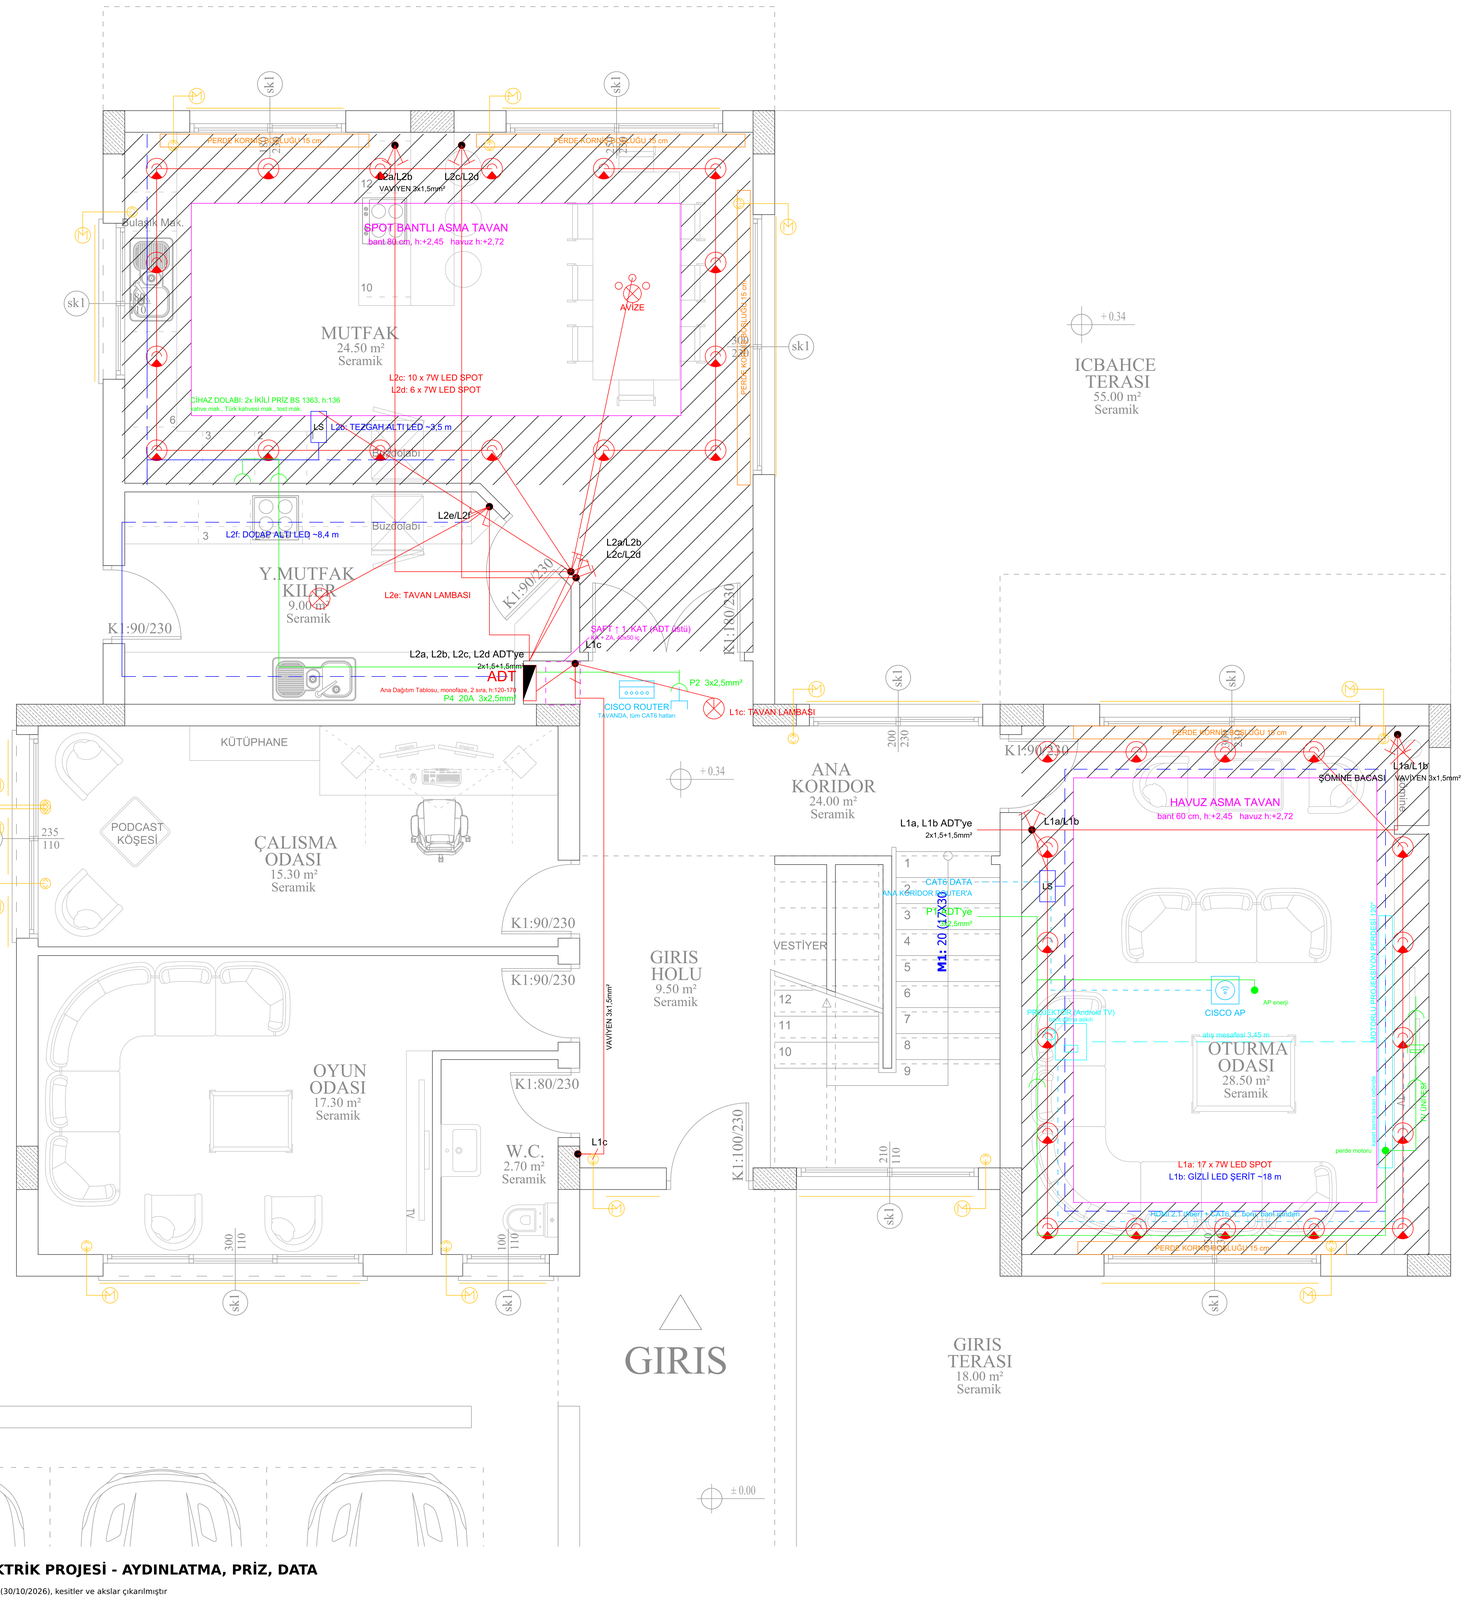



ZEMİN KAT ELEKTRİK PROJESİ - AYDINLATMA, PRİZ, DATA

ÖLÇEK 1/25 mimari altlık P.18 (30/10/2026), kesitler ve akslar çıkarılmıştır

LEJANT

KTEMO standart sembolleri

- Gömme Tip Spot Lamba (İç) - LED 7W, dimlenebilir
- Gizli LED Şerit (havuz kenarı / tezgah altı) 24V, 10 W/m
- LED Sürücü (asma tavan içinde, servis kapaklı)
- Havuz Asma Tavan Kenarı
- Perde Korniş Boşluğu (asma tavanda, döşemeye kadar)
- Asma Tavan Bandı
- Komütatör (Çift) Anahtar
- Komütatör Vaviyen Anahtar (iki yerden kumanda)
- Vaviyen Anahtar (tekli, iki yerden kumanda)
- Avize
- Tavan Lambası
- Tekli Anahtar
- Tavan Tipi Kablosuz Erişim Noktası (Cisco) - data + enerji
- Cisco Router, tavanda (data noktası, ayrı prizli)
- Motorlu Panjur (dış kutulu) - motor noktası
- Panjur Aşağı / Yukarı Anahtarı
- Data Prizi (CAT6)
- Video Projeksiyon Cihazı (tavana askılı, Android TV)
- Motorlu Projeksiyon Perdesi ve Kaset Cebi
- Priz, BS 1363 (UK, G tipi, 13A, anahtarlı)
- Sabit Cihaz Bağlantı Noktası (perde motoru)
- TV Prizi
- Priz Hattı 3x2,5mm² Cu PVC, 5/8" PVC boru
- Aydınlatma Hattı 2x1,5+1,5mm² Cu PVC, 5/8" PVC boru
- Data Hattı CAT6, 1"3/4" PVC boru

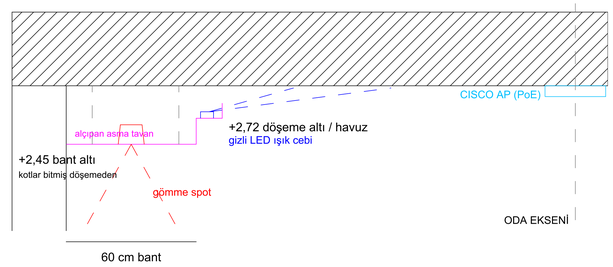

HAVUZ ASMA TAVAN KESİT DETAYI 1/10 (oturma odası, duvardan oda eksenine)

NOTLAR
1. Tesisat MONOFAZE (tek faz, 230V). Anahtarlar h:110 cm, kapının kilit tarafında, aslâ kapı arkasında değil. Aydınlatma lineleri: L1 oturma + ana koridor, L2 mutfak + kiler; harfler anahtar uçlarındır (L2a avize, L2b LED ...), ayrı sigorta değil.

OTURMA ODASI
2. Havuz asma tavan: 60 cm bant, bant altı +2,45, havuz +2,72 (döşeme altı).
3. L1a: 17 gömme spot bant ekseninde, ~1,10 m aralık; KD köşede sömine bacası nedeniyle spot yok. L1b: havuz kenarında gizli LED, sürücü (LS) bantta.
4. Kapı yanında ÇİFT anahtar: L1a spotlar + L1b gizli LED; VAVİYEN, bahçeye bakan kuzey 300/230'un doğusunda da aynı anahtar. Anahtar aslâ kapı arkasına konmaz.
5. Pencere ve sürgü önünde perde korniş boşluğu 15 cm, açıklıktan 30 cm taşar.
6. TV konumu: önüne 120" motorlu perde iner (kaset doğu bandında, duvardan 50 cm). Projektör batı bandına askılı, atış 3.45 m. HDMI 2.1 fiber + CAT6 TV ünitesinden projektöre bant içinden. Perde 12V tetik / RF ile.
7. Cisco AP havuz ortasında: CAT6 + AYRI ENERJİ (P1). Borular beton öncesi döşemeye.

MUTFAK
8. Spot bantı asma tavan: 80 cm bant (spotlar üst dolapların önünde), bant altı +2,45, gizli LED yok. L2c: 10 spot mutfak, L2d: 6 spot yemek tarafı.
9. L2a: yemek masası üzerinde avize; buab beton öncesi döşemeye. Kuzey 180/230, sürme kapı ve doğu 300/230 önünde bantta 15 cm perde korniş boşluğu.
10. L2b: mutfak üst dolaplarının altında LED şerit, sürücü (LS) dolap içinde.
11. Muftakta köşedeki kiler kapısının solunda iki ÇİFT anahtar: L2a avize + L2b LED, L2c + L2d spotlar (kilere geçerken elin altında). Tümü VAVİYEN: aynı ikisi kuzeyde iki cam açıklık arasındaki kolonun iki yanında (kolona buat konmaz; h:120, ada üstü): L2a/L2b batıda, L2c/L2d doğuda. Bahçeye çıkarken bütün ışıklar oradan söner.

11a. Kilerde tavan ortasında tavan lambası (L2e) ve üst dolap altı LED (L2f); ÇİFT anahtarı içeride köşe kapının kilit tarafında h:110.
12a. Güney tezgahın batı ucunda 1,50 m cihaz dolabı (sürgülü kapaklı): tam otomatik kahve mak., Türk kahvesi mak., tost mak.; arka panelde 2 ikili priz h:136, P4.

ANA KORİDOR
11b. ANA KORİDOR tavan lambası L1c, VAVİYEN: ana kapı girişinde solda (hol batı duvarı) ve ADT nişinin ağzında sağ yanda, h:110.
12. ADT koridorun batısındaki dolap nişinde, arka duvarda, alt kenarı h:120 (üst 170): monofaze, 2 sıra sıva üstü tablo (Hager Gamma tipi ~40x50x12 cm): ana şalter, parafudr, kaçak akım (RCD/RCBO), sigortalar. Nişin üstünden 1. kata 40x50 TESİSAT ŞAFTI çıkar: kuvvetli akım (KA) ve zayıf akım (ZA) buradan geçer (E-02). Cisco router TAVANDA; evin data noktası, tüm CAT6 burada. Ağ cihazları data ile birlikte ENERJİ ile de beslenir: yanında tavan prizi (P2). 1. katta ikinci router ANA KORİDOR ortasında tavanda.

PRİZLER
14. Tüm prizler İngiliz standardı: BS 1363 (G tipi, 13A, anahtarlı), tesisat BS 7671.

PANJURLAR
13. Dışa bakan her pencere ve sürme kapıda motorlu panjur (14 adet), dış kutulu; motor kutuda, aşağı/yukarı anahtarı içeride pencere yanında h:110. Hepsi P3.

YÜKLEME CETVELİ (taslak) - ADT, monofaze, şebekeden 2x80A


Devre	Sigorta	Kesit mm²	Devre Adı	Adet	Birim kW	Devre kW	T.f.	Talep kW
L1	10A	1,5	Oturma od. + ana koridor aydınlatma (L1a-L1c)	19	-	0.345	0,4	0.138
L2	10A	1,5	Mutfak + kiler aydınlatma (L2a-L2f)	20	-	0.335	0,5	0.168
P1	16A	2,5	Oturma od. TV ün., projektör, perde, AP	5	-	0.925	0,5	0.463
P2	16A	2,5	Ana koridor router prizi	1	0.060	0.060	1,0	0.060
P3	16A	2,5	Panjur motorları	14	0.120	1.680	0,3	0.504
P4	20A	2,5	Muftak cihaz dolabı (BS 1363)	4	-	3.085	0,5	1.542

VILLA KHAN

ELEKTRİK PROJESİ - MONOFAZE

PAFTA	E-01 ZEMİN KAT ELEKTRİK PROJESİ
MİMARİ ALTLIK	30102026_FINAL DRAFT.dwg (P.18, 30/10/2026)
SEMBOLLER	KTEMO standart lejantı (E-01)
ÖLÇEK	1/25, 1/10 - A0
REVİZYON	E.01 TASLAK 30/10/2026

Ön tasarımdır. Oda vizesi için yetkili elektrik mühendisinin hesap ve imzası gerekir.

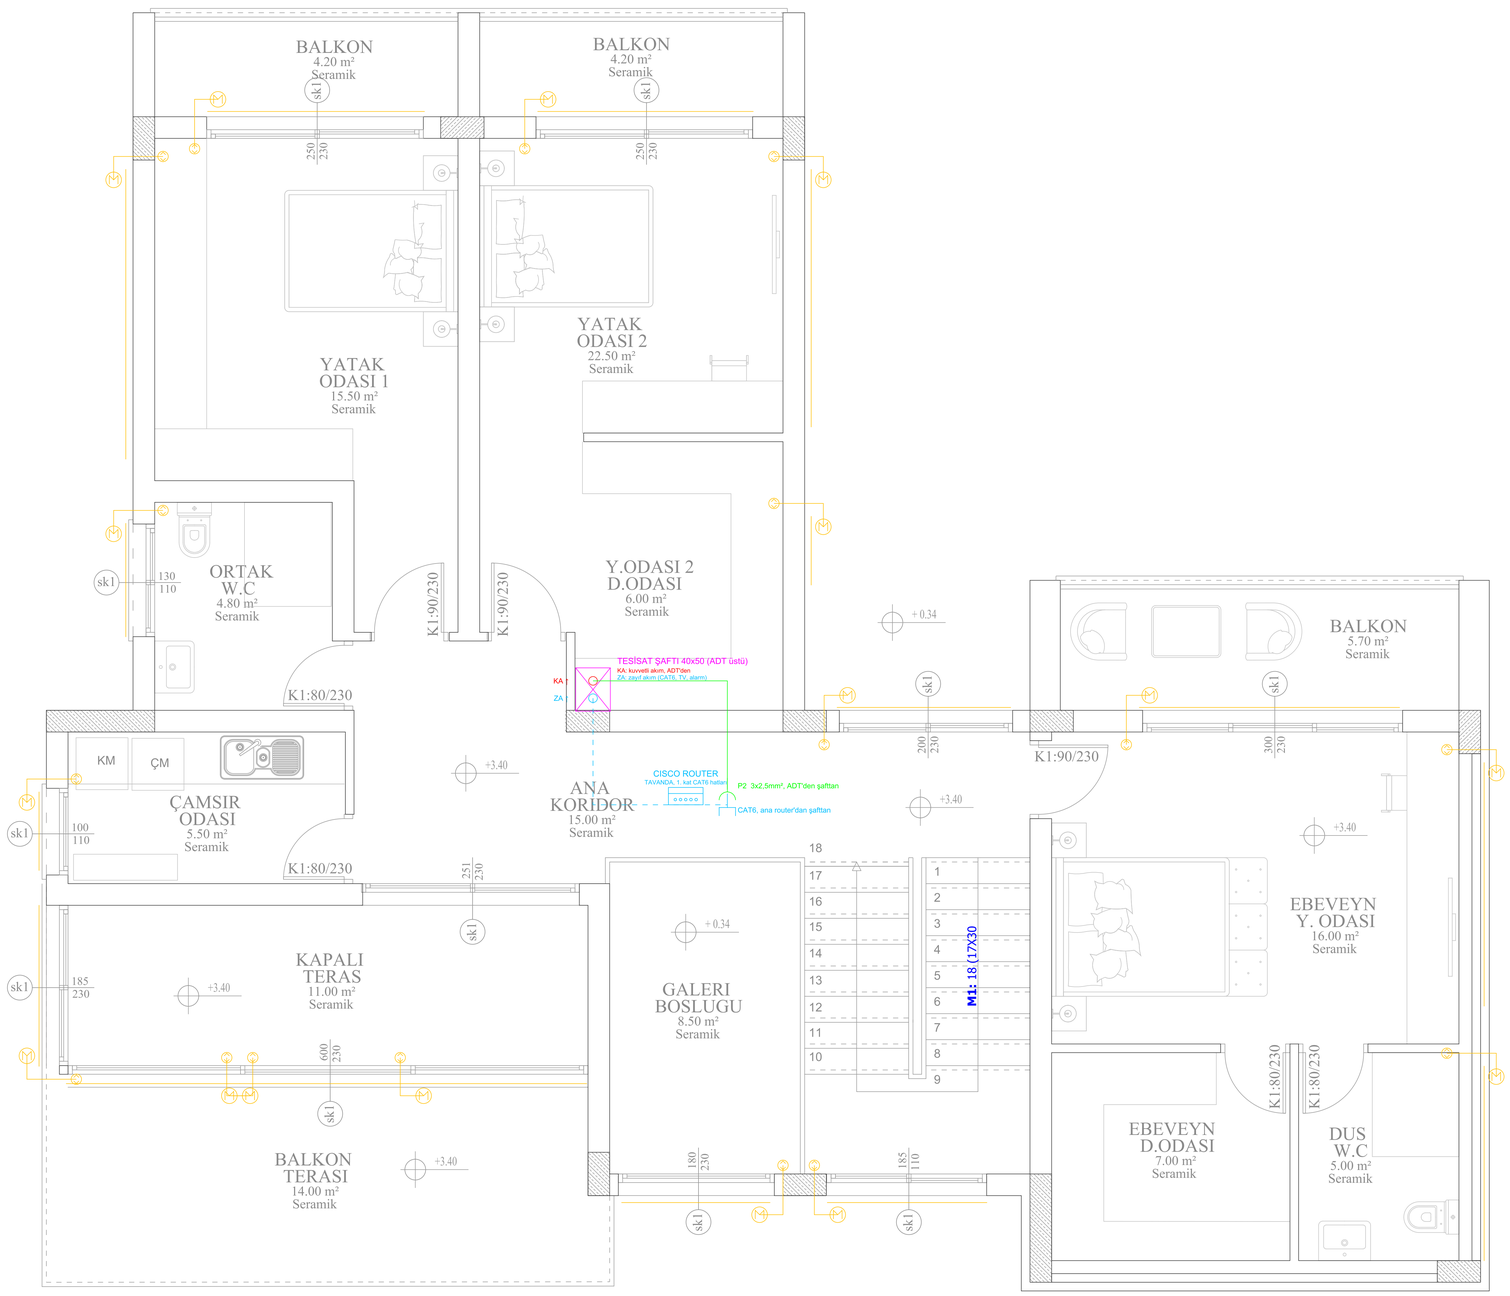

LEJANT

KTEMO standart sembolleri

- Gömme Tip Spot Lamba (İç) - LED 7W, dimlenebilir
- Gizli LED Şerit (havuz kenarı / tezgah altı) 24V, 10 W/m
- LED Sürücü (asma tavan içinde, servis kapaklı)
- Havuz Asma Tavan Kenarı
- Perde Korniş Boşluğu (asma tavanda, döşemeye kadar)
- Asma Tavan Bandı
- Komütatör (Çift) Anahtar
- Komütatör Vaviyen Anahtar (iki yerden kumanda)
- Vaviyen Anahtar (tekli, iki yerden kumanda)
- Avize
- Tavan Lambası
- Tekli Anahtar
- Tavan Tipi Kablosuz Erişim Noktası (Cisco) - data + enerji
- Cisco Router, tavanda (data noktası, ayrı prizli)
- Motorlu Panjur (dış kutulu) - motor noktası
- Panjur Aşağı / Yukarı Anahtarı
- Data Prizi (CAT6)
- Video Projeksiyon Cihazı (tavana askılı, Android TV)
- Motorlu Projeksiyon Perdesi ve Kaset Cebi
- Priz, BS 1363 (UK, G tipi, 13A, anahtarlı)
- Sabit Cihaz Bağlantı Noktası (perde motoru)
- TV Prizi
- Priz Hattı 3x2,5mm² Cu PVC, 5/8" PVC boru
- Aydınlatma Hattı 2x1,5+1,5mm² Cu PVC, 5/8" PVC boru
- Data Hattı CAT6, 1"3/4" PVC boru

NOTLAR

1. Tesisat MONOFAZE (tek faz, 230V). Lejant E-01 ile aynıdır.

TESİSAT ŞAFTI

2. Zemin kat ADT nişinin tam üstünde, Y.ODASI 2 D.ODASI'nın güneybatı köşesinde, kolona dayalı 40x50 cm (iç) şaft; döşemede aynı ölçüde boşluk bırakılacak. Kapaklı, katlar arası yangın durdurucu ile kapatılır.
3. KA (kuvvetli akım): ADT'den 1. kat linyeleri ve P2 router prizi.
   ZA (zayıf akım): CAT6 data, TV, alarm; kuvvetli akımdan ayrı boruda.
4. Giyinme odasının güney dolap dizisi şaftın doğusundan başlar.

ANA KORİDOR

5. Cisco router koridor ortasında TAVANDA, yanında tavan prizi (P2) ve CAT6; zemin kattaki ana router'a şaft üzerinden bağlı.

PANJURLAR

6. Dışa bakan her pencere ve sürme kapıda motorlu panjur (17 adet), dış kutulu; motor kutuda, aşağı/yukarı anahtarı içeride pencere yanında h:110. Hepsi P3.
7. Oda aydınlatma ve prizleri sonraki revizyonda işlenecektir.

VILLA KHAN

ELEKTRİK PROJESİ - MONOFAZE

PAFTA	E-02 1. KAT ELEKTRİK PROJESİ
MİMARİ ALTLIK	30102026_FINAL DRAFT.dwg (P.18, 30/10/2026)
SEMBOLLER	KTEMO standart lejantı (E-01)
ÖLÇEK	1/25 - A0
REVİZYON	E.01 TASLAK 30/10/2026

Ön tasarımdır. Oda vizesi için yetkili elektrik mühendisinin hesap ve imzası gerekir.

1. KAT ELEKTRİK PROJESİ - ŞAFT, DATA, PANJUR

ÖLÇEK 1/25 mimari altlık P.18 (30/10/2026), kesitler ve akslar çıkarılmıştır