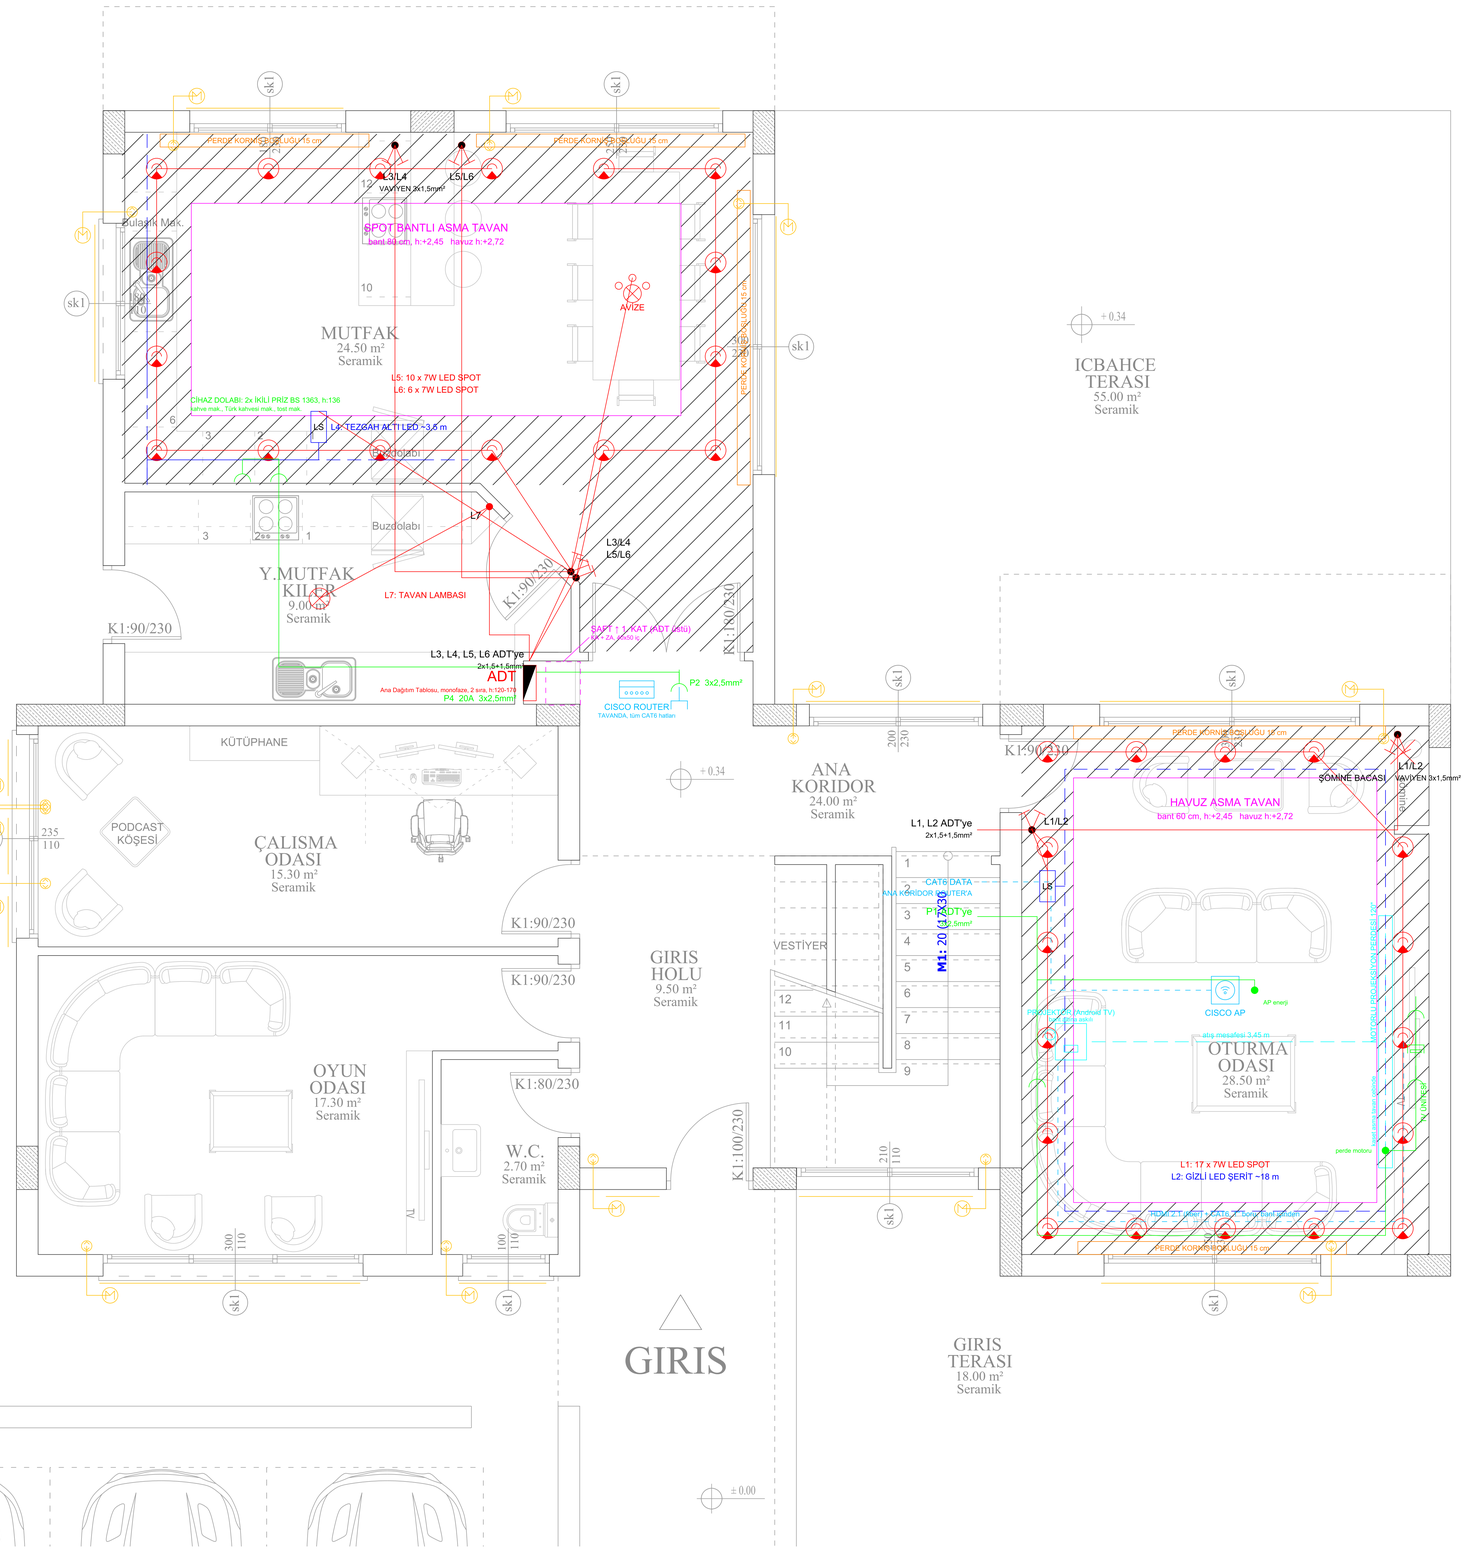



ZEMİN KAT ELEKTRİK PROJESİ - AYDINLATMA, PRİZ, DATA

ÖLÇEK 1/25 mimari altlık P.18 (30/10/2026), kesitler ve akslar çıkarılmıştır

LEJANT

KTEMO standart sembolleri

- Gömme Tip Spot Lamba (İç) - LED 7W, dimlenebilir
- Gizli LED Şerit (havuz kenarı / tezgah altı) 24V, 10 W/m
- LED Sürücü (asma tavan içinde, servis kapaklı)
- Havuz Asma Tavan Kenarı
- Perde Korniş Boşluğu (asma tavanda, döşemeye kadar)
- Asma Tavan Bandı
- Komütatör (Çift) Anahtar
- Komütatör Vaviyen Anahtar (iki yerden kumanda)
- Avize
- Tavan Lambası
- Tekli Anahtar
- Tavan Tipi Kablosuz Erişim Noktası (Cisco) - data + enerji
- Cisco Router, tavanda (data noktası, ayrı prizli)
- Motorlu Panjur (dış kutulu) - motor noktası
- Panjur Aşağı / Yukarı Anahtarı
- Data Prizi (CAT6)
- Video Projeksiyon Cihazı (tavana askılı, Android TV)
- Motorlu Projeksiyon Perdesi ve Kaset Cebi
- Priz, BS 1363 (UK, G tipi, 13A, anahtarlı)
- Sabit Cihaz Bağlantı Noktası (perde motoru)
- TV Prizi
- Priz Hattı 3x2,5mm² Cu PVC, 5/8" PVC boru
- Aydınlatma Hattı 2x1,5+1,5mm² Cu PVC, 5/8" PVC boru
- Data Hattı CAT6, 1"3/4" PVC boru
- Spot konmayan nokta

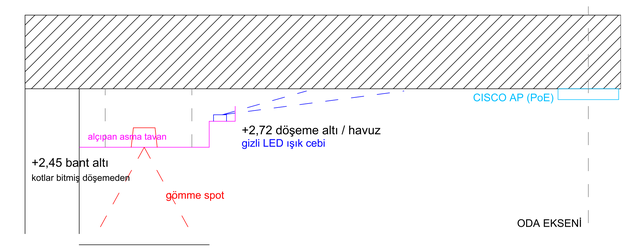

HAVUZ ASMA TAVAN KESİT DETAYI 1/10 (oturma odası, duvardan oda eksenine)

NOTLAR
1. Tesisat MONOFAZE (tek faz, 230V). Anahtarlar h:110 cm, kapının kilit tarafında.
OTURMA ODASI
2, Havuz asma tavan: 60 cm bant, bant altı +2,45, havuz +2,72 (döşeme altı).
3, L1: 17 gömme spot bant ekseninde, ~1,10 m aralık; KD köşede şömine bacası nedeniyle spot yok. L2: havuz kenarında gizli LED, sürücü (L5) bantta.
4. Kapı yanında ÇİFT anahtar: L1 spotlar + L2 gizli LED; VAVİYEN, bahçeye bakan kuzey 300/230'un doğusunda da aynı anahtar. Anahtar asla kapı arkasına konmaz.
5. Pencere ve sürgü önünde perde korniş boşluğu 15 cm, açıklıktan 30 cm taşar.
6. TV konumu; önüne 120° motorlu perde iner (kaset doğu bandında, duvardan 50 cm). Projektör batı bandına askılı, ataş 3,45 m. HDMI 2.1 fiber + CAT6 TV ünitesinden projektöre bant içinden. Perde 12V tetik / RF ile.
7. Cisco AP havuz ortasında: CAT6 + AYRI ENERJİ (P1). Bonjları beton öncesi döşemeye.
MUTFAK
8. Spot bantlı asma tavan: 80 cm bant (spotlar üst dolapların önünde), bant altı +2,45, gizli LED yok. L5: 10 spot mutfak, L6: 6 spot yemek tarafı.
9. L3: yemek masası üzerinde avize; buab beton öncesi döşemeye. Kuzey 180/230, sürme kapı ve doğu 300/230 önünde bantta 15 cm perde kornişi boşluğu.
10, L4: üst dolapların altında LED şerit ~3,5 m, sürücü (L5) dolap içinde,
11. Mutfakta köşedeki kiler kapısının solunda iki ÇİFT anahtar: L3 avize + L4 LED, L5 + L6 spotlar (kilere geçerken elin altında). Tümü VAVİYEN: aynı ikisi kuzeyde iki cam açıklık arasındaki kolonun iki yanında (kolona buat konmaz; h:120, ada üstü): L3/L4 batıda, L5/L6 doğuda. Bahçeye çıkarken bütün ışıklar oradan söner.
11a. Kilerde tavan ortasında tavan lambası (L7), anahtarı içeride köşe kapının kilit tarafında h:110.
12a. Güney tezgahın batı ucunda 1,50 m cihaz dolabı (sürgülü kapaklı): tam otomatik kahve mak., Türk kahvesi mak., tost mak.; arka panelde 2 ikili priz h:136, P4.
ANA KORİDOR
12. ADT koridorun batısındaki dolap nişinde, arka duvarda, alt kenarı h:120 (üst 170): monofaze, 2 sıra sıva üstü tablo (Hager Gamma tipi ~40x50x12 cm): ana şalter, parafudr, kaçak akım (RCD/RCBO), sigortalar. Nişin üstünden 1. kata 40x50 TEŞİSAT ŞAFTI çıkar; kuvvetli akım (KA) ve zayıf akım (ZA) buradan geçer (E-02). Cisco router TAVANDA; evin data noktası, tüm CAT6 burada. Ağ cihazları data ile birlikte ENERJİ ile de beslenir; yanında tavan prizi (P2). 1. katta ikinci router ANA KORİDOR ortasında tavanda.
PRİZLER
14. Tüm prizler İngiliz standardı: BS 1363 (G tipi, 13A, anahtarlı), tesisat BS 7671.
PANJURLAR
13. Dışa bakan her pencere ve sürme kapıda motorlu panjur (14 adet), dış kutulu; motor kutuda, aşağı/yukarı anahtarı içeride pencere yanında h:110. Hepsi P3.

YÜKLEME CETVELİ (taslak) - ADT, monofaze, şebekeden 2x80A


Devre	Sigorta	Kesit mm²	Devre Adı	Adet	Birim kW	Devre kW	T.f.	Talep kW
L1	10A	1,5	Oturma od. spotlar	17	0.007	0.119	0,4	0.048
L2	10A	1,5	Oturma od. gizli LED	1	0.211	0.211	0,4	0.084
L3	10A	1,5	Mutfak avize	1	0.065	0.065	0,5	0.033
L4	10A	1,5	Mutfak tezgah altı LED	1	0.042	0.042	0,5	0.021
L5	10A	1,5	Mutfak spotlar (mutfak)	10	0.007	0.070	0,5	0.035
L6	10A	1,5	Mutfak spotlar (yemek)	6	0.007	0.042	0,5	0.021
L7	10A	1,5	Kiler tavan lambası	1	0.015	0.015	0,5	0.007
P1	16A	2,5	Oturma od. TV ün., projektör, perde, AP	5	-	0.925	0,5	0.463
P2	16A	2,5	Ana koridor router prizi	1	0.060	0.060	1,0	0.060
P3	16A	2,5	Panjur motorları	14	0.120	1.680	0,3	0.504
P4	20A	2,5	Mutfak cihaz dolabı (BS 1363)	4	-	3.085	0,5	1.542

VILLA KHAN

ELEKTRİK PROJESİ - MONOFAZE

PAFTA	E-01 ZEMİN KAT ELEKTRİK PROJESİ
MİMARİ ALTLIK	30102026_FINAL DRAFT.dwg (P.18, 30/10/2026)
SEMBOLLER	KTEMO standart lejantı (E-01)
ÖLÇEK	1/25, 1/10 - A0
REVİZYON	E.01 TASLAK 30/10/2026

Ön tasarımdır. Oda vizesi için yetkili elektrik mühendisinin hesap ve imzası gerekir.

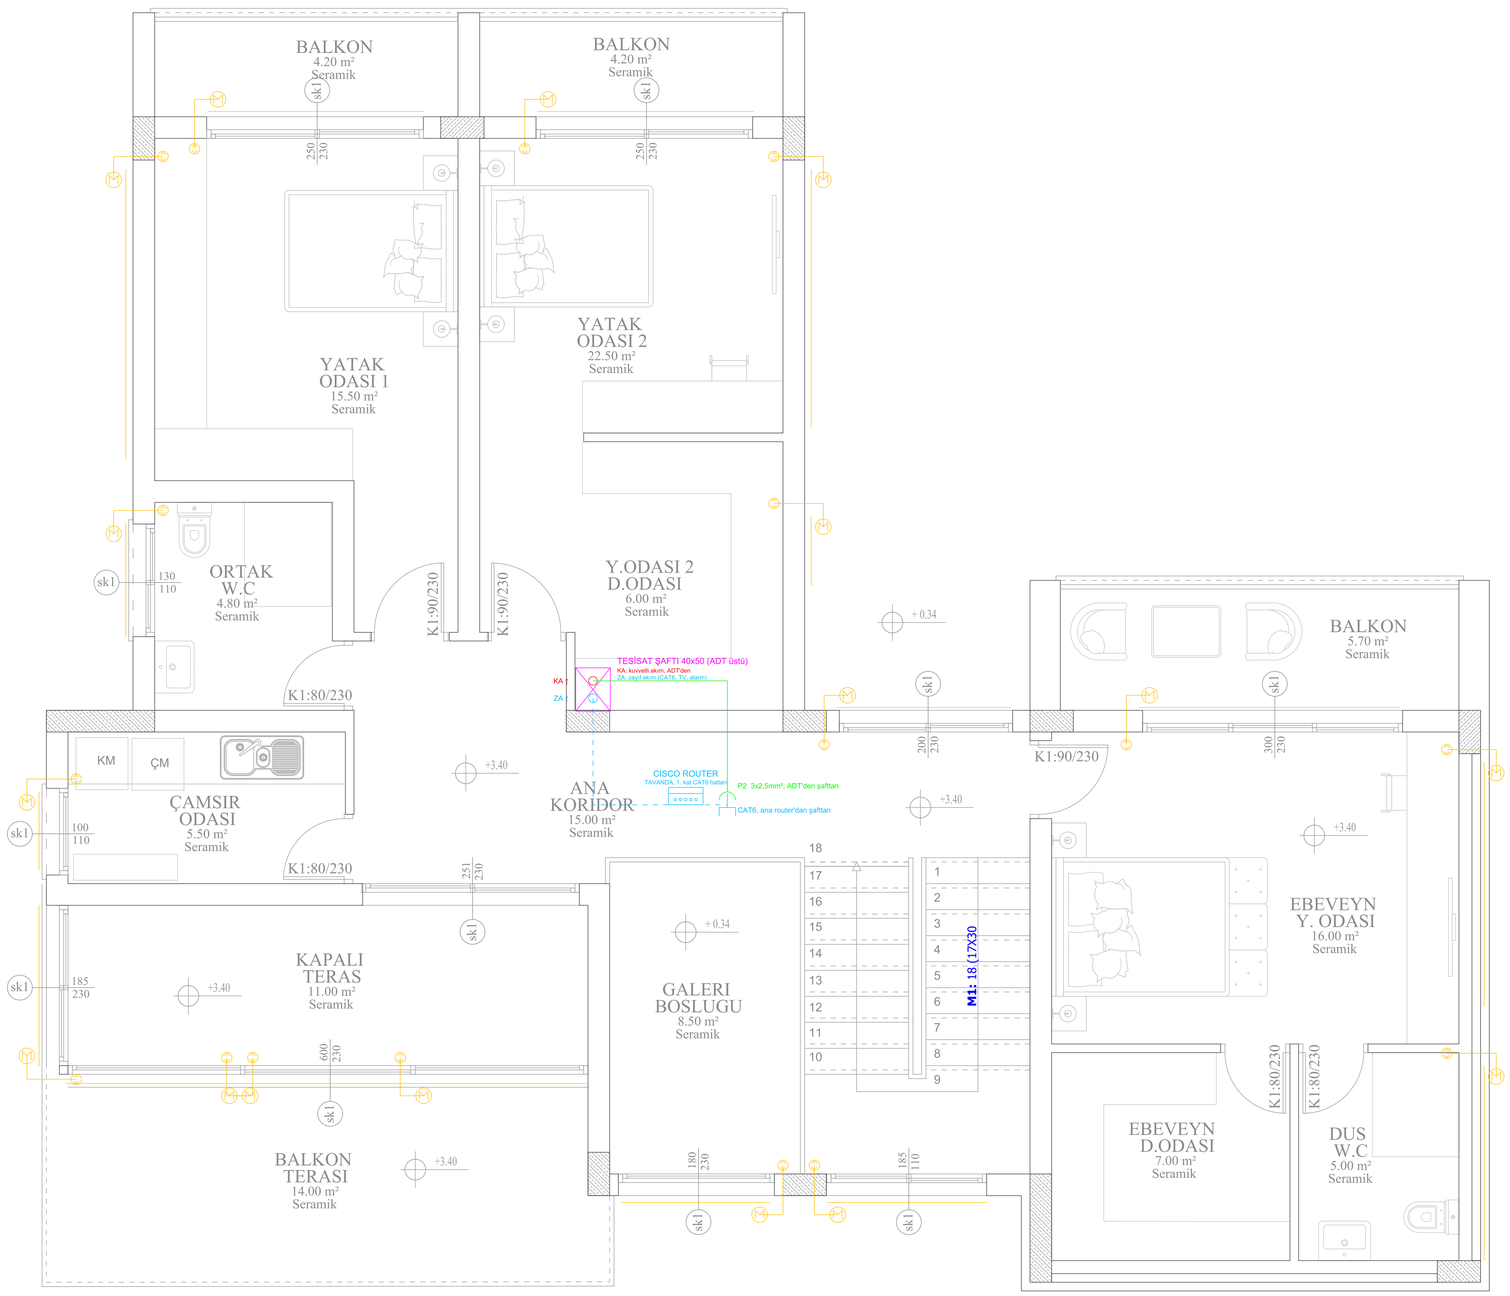

LEJANT

KTEMO standart sembolleri

- Gömme Tip Spot Lamba (İç) - LED 7W, dimlenebilir
- Gizli LED Şerit (havuz kenarı / tezgah altı) 24V, 10 W/m
- LED Sürücü (asma tavan içinde, servis kapaklı)
- Havuz Asma Tavan Kenarı
- Perde Korniş Boşluğu (asma tavanda, döşemeye kadar)
- Asma Tavan Bandı
- Komütatör (Çift) Anahtar
- Komütatör Vaviyen Anahtar (iki yerden kumanda)
- Avize
- Tavan Lambası
- Tekli Anahtar
- Tavan Tipi Kablosuz Erişim Noktası (Cisco) - data + enerji
- Cisco Router, tavanda (data noktası, ayrı priz)
- Motorlu Panjur (dış kutulu) - motor noktası
- Panjur Aşağı / Yukarı Anahtarı
- Data Prizi (CAT6)
- Video Projeksiyon Cihazı (tavana askılı, Android TV)
- Motorlu Projeksiyon Perdesi ve Kaset Cebi
- Priz, BS 1363 (UK, G tipi, 13A, anahtarlı)
- Sabit Cihaz Bağlantı Noktası (perde motoru)
- TV Prizi
- Priz Hattı 3x2,5mm² Cu PVC, 5/8" PVC boru
- Aydınlatma Hattı 2x1,5+1,5mm² Cu PVC, 5/8" PVC boru
- Data Hattı CAT6, 1"3/4" PVC boru
- Spot konmayan nokta

NOTLAR

1. Tesisat MONOFAZE (tek faz, 230V). Lejant E-01 ile aynıdır.

TESİSAT ŞAFTI

2. Zemin kat ADT nişinin tam üstünde, Y.ODASI 2 D.ODASI'nın güneybatı köşesinde, kolona dayalı 40x50 cm (iç) şaft; döşemede aynı ölçüde boşluk bırakılacak. Kapaklı, katlar arası yangın durdurucu ile kapatılır.
3. KA (kuvvetli akım): ADT'den 1. kat linyeleri ve P2 router prizi.
   ZA (zayıf akım): CAT6 data, TV, alarm; kuvvetli akımdan ayrı boruda.
4. Giyinme odasının güney dolap dizisi şaftın doğusundan başlar.

ANA KORİDOR

5. Cisco router koridor ortasında TAVANDA, yanında tavan prizi (P2) ve CAT6; zemin kattaki ana router'a şaft üzerinden bağlı.

PANJURLAR

6. Dışa bakan her pencere ve sürme kapıda motorlu panjur (17 adet), dış kutulu; motor kutuda, aşağı/yukarı anahtarı içeride pencere yanında h:110. Hepsi P3.
7. Oda aydınlatma ve prizleri sonraki revizyonda işlenecektir.

VILLA KHAN

ELEKTRİK PROJESİ - MONOFAZE

PAFTA	E-02 1. KAT ELEKTRİK PROJESİ
MİMARİ ALTLIK	30102026_FINAL DRAFT.dwg (P.18, 30/10/2026)
SEMBOLLER	KTEMO standart lejantı (E-01)
ÖLÇEK	1/25 - A0
REVİZYON	E.01 TASLAK 30/10/2026

Ön tasarımdır. Oda vizesi için yetkili elektrik mühendisinin hesap ve imzası gerekir.

1. KAT ELEKTRİK PROJESİ - ŞAFT, DATA, PANJUR

ÖLÇEK 1/25 mimari altlık P.18 (30/10/2026), kesitler ve akslar çıkarılmıştır